



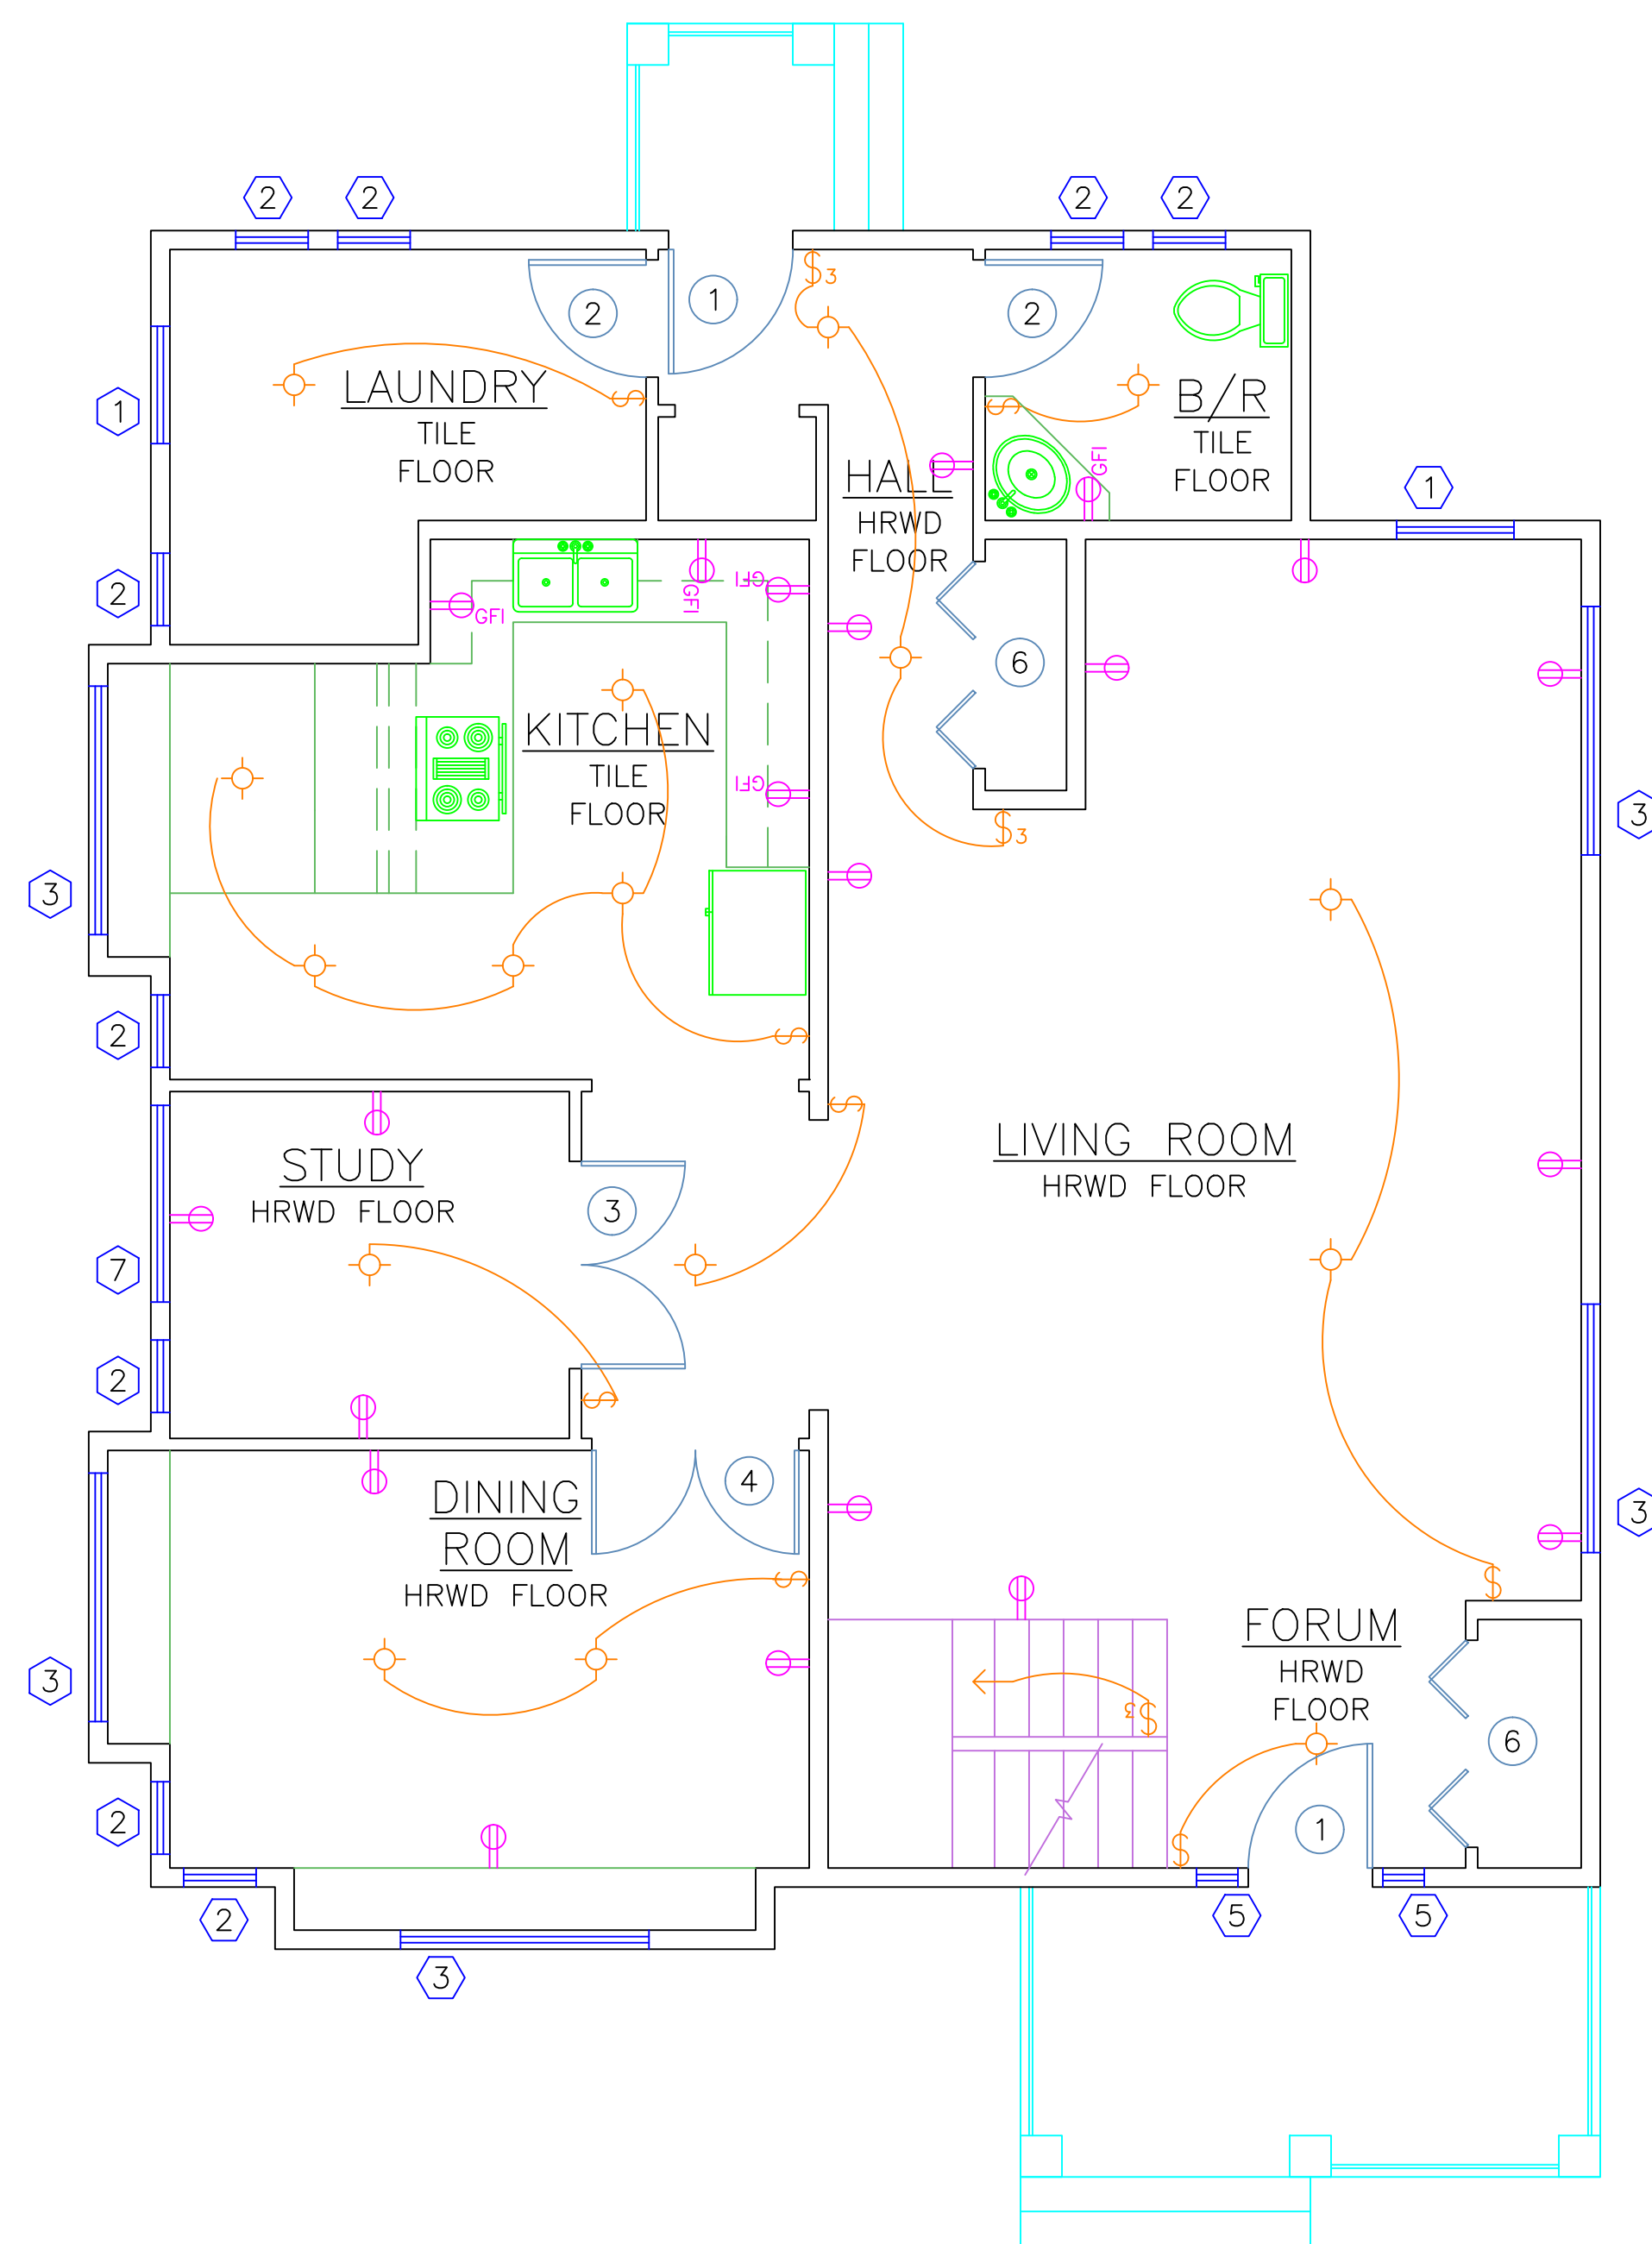

1 FIRST FLOOR PLAN  
SCALE: 1/4"=1'

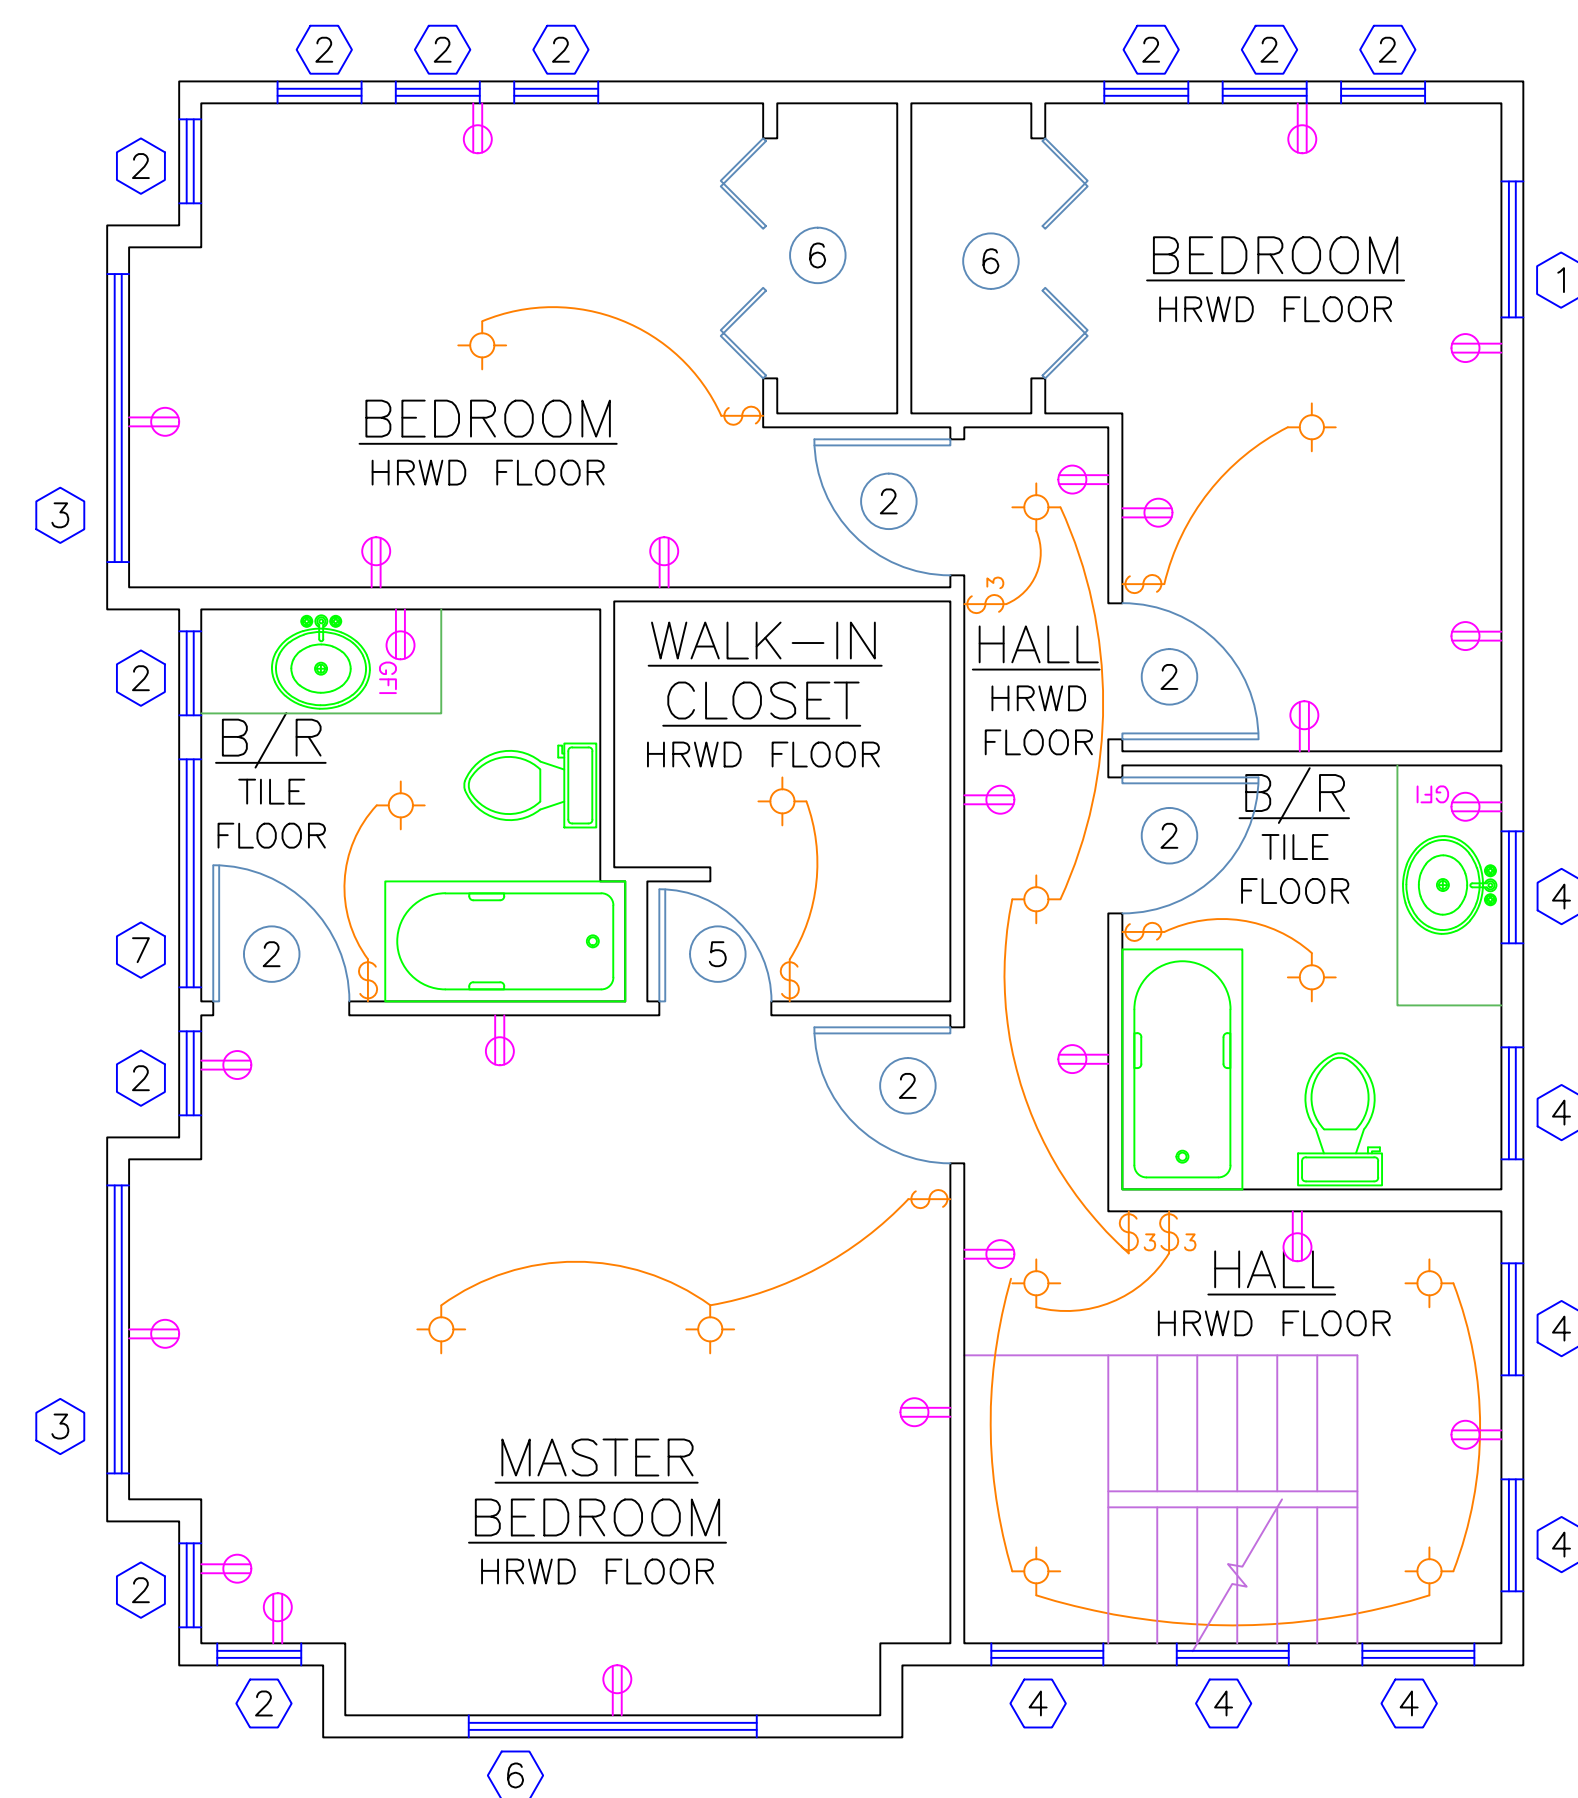

2 SECOND FLOOR PLAN  
SCALE: 1/4"=1'

### GENERAL NOTES:

1. FOUNDATION VENTILATION EQUAL TO 1 SF. OF NET OPENING FOR EACH 150 S.F. OF UNDER FLOOR AREA. ALL FOUNDATION TO COMPLY TO CURRENT UNIFORM BUILDING STANDARDS.
2. VERIFY ALL DIMENSIONS AND CONDITIONS BEFORE BUILDING OR STARTING CONSTRUCTION. NOTIFY THE DESIGNER IMMEDIATELY OF ANY DISCREPANCY OR VARIATION.
3. VERIFY ROUGH OPENINGS AND FRAMING REQUIREMENTS PRIOR TO FRAMING.
4. INTERIOR OF HOUSE IS TO BE PAINTED WHITE WITH 3" OAK BASE BOARD (SEE DETAIL) & 4" OAK COVES AT ALL JUNCTIONS BETWEEN WALL & CEILING OR BEAMS & CEILING (SEE DETAIL).
5. ALL EXTERIOR WALL ARE TO BE 2"x6" FRAMING. INTERIOR WALLS ARE TO BE 2"x4" FRAMING AND ARE NO LOAD BARRING UNLESS OTHERWISE SPECIFIED. ALL HEADERS ON FIRST FLOOR ARE TO BE DBL. 2"x10" AND ALL HEADERS ON SECOND FLOOR ARE TO BE DBL. 2"x8".
6. ROOFING SYSTEM IS TO BE ENGINEERED TRUSSES. OVERHANG IS TO BE 2' AT ALL EAVES.
7. STUCCO SIDING IS TO BE QUIKRETE QUIKWALL FIBERGLASS REINFORCED STUCCO (FRS) #1200 APPLICATION IS TO MEET ALL LOCAL CODE REQUIREMENTS.
8. METAL ROOFING IS TO BE MCELROYMETAL, INC. MASTERLOK-90 STRUCTURAL STANDING SEAM ROOF SYSTEM.

### DOOR SCHEDULE

| SYM.                    | WIDTH | HEIGHT | STYLE        | REF#    | MANUFACTURER | QTY | COST   | TOTAL     |
|-------------------------|-------|--------|--------------|---------|--------------|-----|--------|-----------|
| 1                       | 3'    | 6'-8"  | TWO PANEL    | TS 3010 | TRU STYLE    | 2   | 189.00 | \$378.00  |
| 2                       | 3'    | 6'-8"  | TWO PANEL    | TS 3010 | TRU STYLE    | 7   | 189.00 | \$1323.00 |
| 3                       | 5'    | 6'-8"  | FRENCH DOORS | FL 301  | TRU STYLE    | 1   | 310.00 | \$310.00  |
| 4                       | 5'    | 6'-8"  | FRENCH DOORS | FL 1000 | TRU STYLE    | 1   | 329.00 | \$329.00  |
| 5                       | 2'-4" | 6'-8"  | ONE PANEL    | TS 3010 | TRU STYLE    | 1   | 189.00 | \$189.00  |
| 6                       | 5'    | 6'-8"  | BI-FOLD      | BF 5068 | TRU STYLE    | 4   | 119.00 | \$476.00  |
| ESTIMATED COST OF DOORS |       |        |              |         |              |     |        | \$3005.00 |

### WINDOW SCHEDULE

| SYM.                      | WIDTH  | HEIGHT    | STYLE     | REF#    | MANUFACTURER | QTY | COST   | TOTAL     |
|---------------------------|--------|-----------|-----------|---------|--------------|-----|--------|-----------|
| 1                         | 2'-10" | 4'-0 1/2" | CASEMENT  | TW28310 | ANDERSEN     | 3   | 169.00 | \$507.00  |
| 2                         | 1'-9"  | 4'-0 1/2" | CASEMENT  | CN14    | ANDERSEN     | 20  | 159.00 | \$3180.00 |
| 3                         | 6'-0"  | 4'-0 1/2" | CASEMENT  | C34     | ANDERSEN     | 7   | 249.00 | \$1743.00 |
| 4                         | 2'-4"  | 2'-0"     | CASEMENT  | CW12    | ANDERSEN     | 7   | 159.00 | \$1113.00 |
| 5                         | 1'-0"  | 4'-5 1/2" | TILT-WASH | DHP1041 | ANDERSEN     | 2   | 109.00 | \$218.00  |
| 6                         | 6'-0"  | 3'-1 1/2" | CASEMENT  | C33     | ANDERSEN     | 1   | 229.00 | \$229.00  |
| 7                         | 4'-9"  | 4'-0 1/2" | CASEMENT  | W24     | ANDERSEN     | 2   | 189.00 | \$378.00  |
| ESTIMATED COST OF WINDOWS |        |           |           |         |              |     |        | \$7368.00 |

